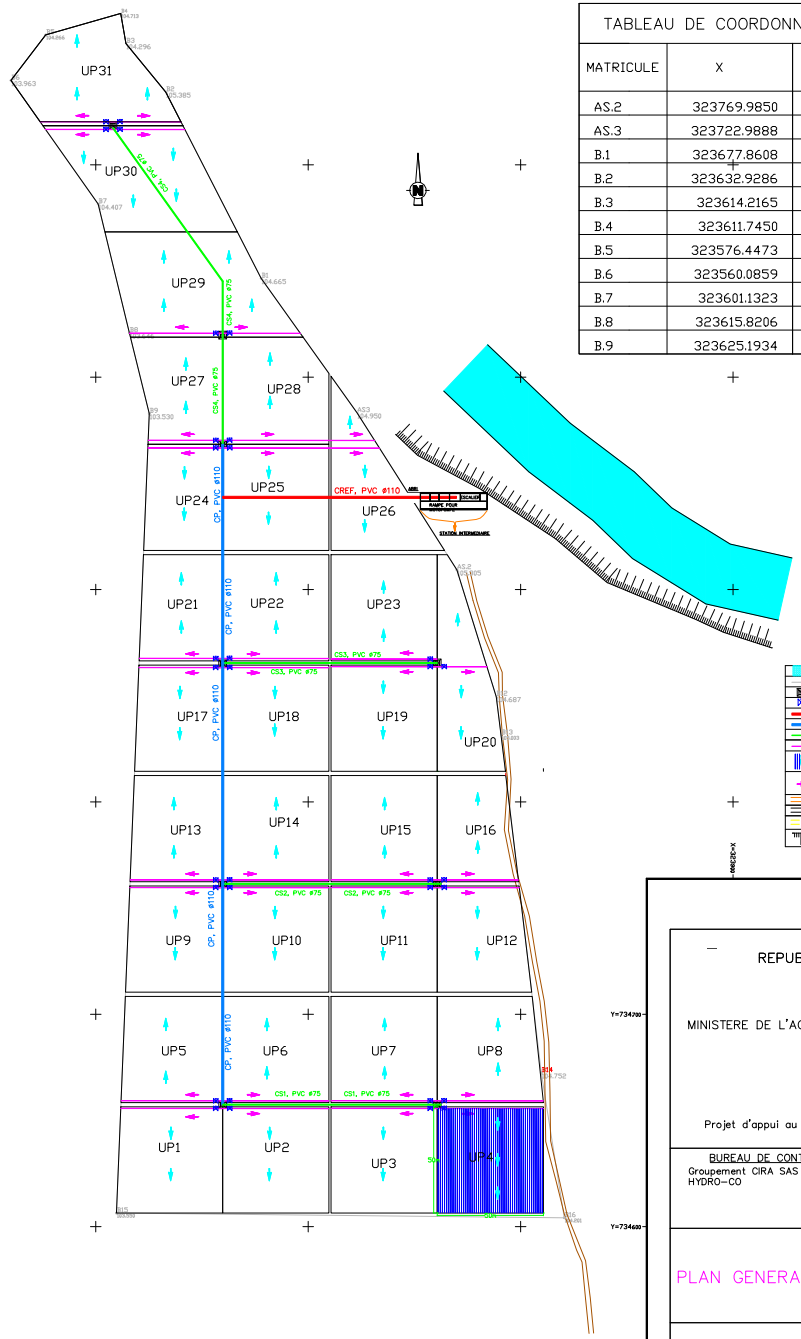

TABLEAU DE COORDONNEES DE LA POLYGONALE			
MATRICULE	X	Y	Z
AS.2	323769.9850	734909.2840	105.3051
AS.3	323722.9888	734983.2345	104.9502
B.1	323677.8608	735046.5157	104.6652
B.2	323632.9286	735134.2971	105.3852
B.3	323614.2165	735157.1050	104.2962
B.4	323611.7450	735171.2792	104.7132
B.5	323576.4473	735161.1886	104.2662
B.6	323560.0859	735139.7495	103.9632
B.7	323601.1323	735081.5364	104.4072
B.8	323615.8206	735020.8717	103.6462
B.9	323625.1934	734982.8689	103.5302

LEGENDE

- FLEUVE N°2
- Limite du séminaire
- Tête de Contrôle
- Vanne
- Conduite de refoulement L= 1100m
- Conduite primaire L= 311
- Conduite secondaire L= 624 et rampe (450
- Lignes de goutteurs et sens d'écoulement
- Sens d'écoulement dans les
- Porte d'arrosage
- Piste d'accès
- Piste périmétrale
- Drain ou Fossé
- TALUS

REPUBLIQUE DE CÔTE D'IVOIRE

Union – Discipline – Travail

MINISTERE DE L'AGRICULTURE ET DU DEVELOPPEMENT RURAL

Projet d'appui au developpement des filières manioc et maraichers

BUREAU DE CONTROLE	OBJET
Groupement CIRA SAS – HYDRO-CO	Travaux d'amenagement de perimetre maraichers, irrigue au systeme goutte à goutte, site de SOUNGASSOU 1, sous préfecture de DIMBOKRO.

PLAN GENERAL D'AMENAGEMENT

Décembre 2020

Echelle 1/1000

Sup.levé: 07.72ha

Sup.am: 07.40ha

DATE	N°	MODIFICATIONS
18/02/2021	A	Changement de position de la station de pompage et drains d'évacuation des eaux

ABEDA SARL
Etudes et Services
TEL : (+225) 20 22 24 24
Fax : (+225) 20 22 05 06
E-mail : abeda@aviso.ci