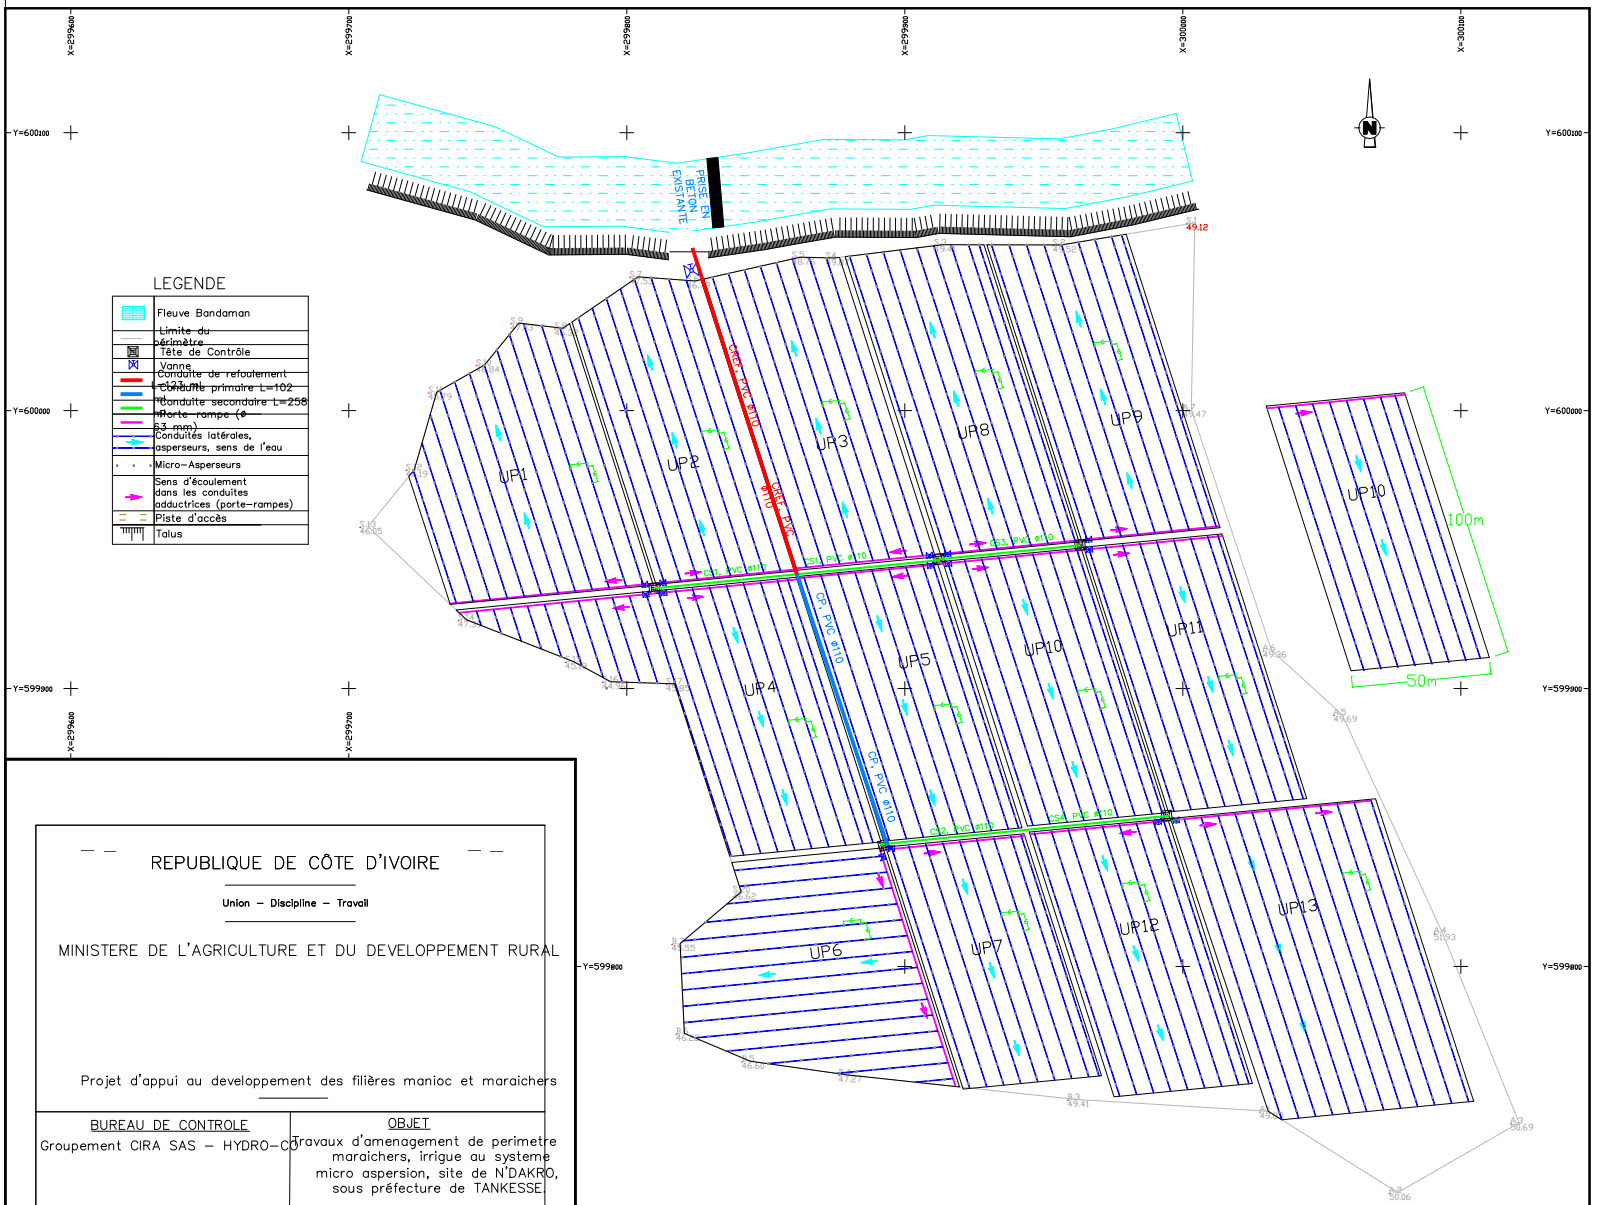

REPUBLIQUE DE CÔTE D'IVOIRE

Union – Discipline – Travail

MINISTERE DE L'AGRICULTURE ET DU DEVELOPPEMENT RURAL

Projet d'appui au developpement des filières manioc et maraichers

BUREAU DE CONTROLE	OBJET
Groupement CIRA SAS – HYDRO-CO	Travaux d'amenagement de perimetre maraichers, irrigue au systeme micro aspersion, site de N'DAKRO, sous préfecture de TANKESSE.

PLAN GENERAL D'AMENAGEMENT

Décembre 2020

Echelle 1/1000

Sup.levée: 08.11ha

Sup.am: 07.51ha

DATE	N°	MODIFICATIONS
23/04/2021	A	Changement de position de la station de pompage et décalage des conduites de refoulement et primaire

ABEDA SARL
ETUDES ET TRAVAUX
TEL : (+225) 20 22 24 24
Fax : (+225) 20 22 05 05
E-mail : abeda@aviso.ci

TABBLEAU DE COORDONNEES DES SOMMETS DE LA POLYGONALE

MATRICULE	X	Y	Z
S.1	300001.2499	600067.2472	49.1217
S.2	299953.2163	600059.3090	49.5219
S.3	299910.5497	600059.3861	49.4105
S.4	299871.5455	600054.6065	49.8727
S.5	299859.3632	600054.8989	48.7572
S.6	299821.5247	600046.3474	46.7263
S.7	299800.9953	600047.8352	47.5265
S.8	299773.9801	600029.3383	46.3207
S.9	299758.1121	600031.1741	47.0336
S.10	299745.7456	600016.0929	46.8393
S.11	299728.5637	600006.3202	45.7941