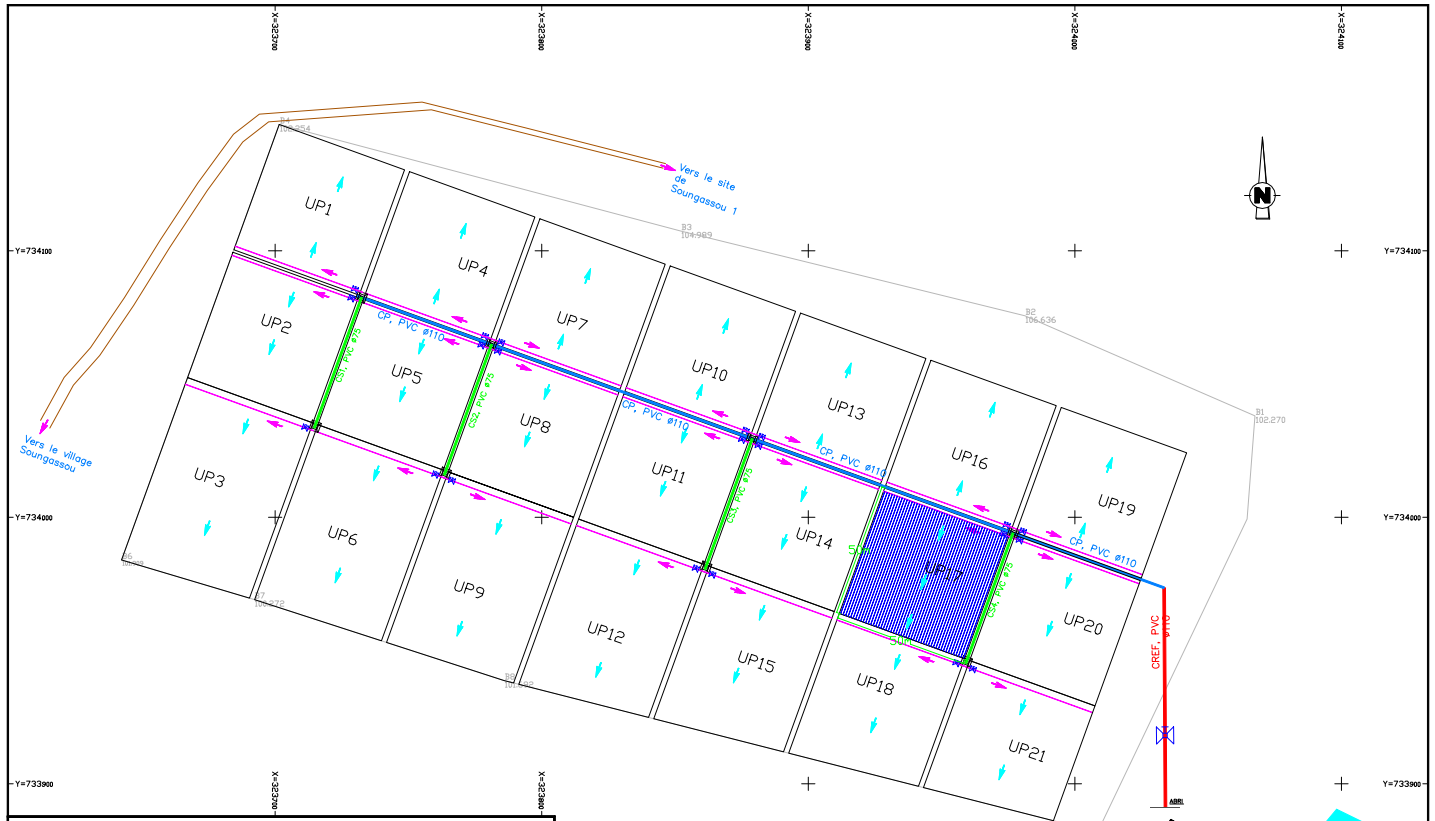

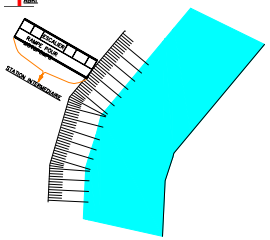

REPUBLIQUE DE CÔTE D'IVOIRE

Union – Discipline – Travail

MINISTERE DE L'AGRICULTURE ET DU DEVELOPPEMENT RURAL

Projet d'appui au developpement des filières manioc et maraichers

BUREAU DE CONTROLE	OBJET
Groupement CIRA SAS – HYDRO–CO	Travaux d'amenagement de perimetre maraichers, irrigue au systeme californien site de SOUNGASSOU 3, sous préfecture de DIMBOKRO.

PLAN GENERAL D'AMENAGEMENT

Décembre 2020

Echelle 1/1000

Sup.lévée: 06.85ha

Sup.am: 05.65ha

DATE	N°	MODIFICATIONS
10/04/2021	A	Repositionnement de la piste d'accès

ABEDA SARL
ETUDES ET TRAVAUX
TEL : (+225) 20 22 24 24
Fax : (+225) 20 22 05 05
E-mail : abeda@aviso.ci

LEGENDE

- FLEUVE N'ZI
- Limite du périmètre
- Tête de Contrôle
- Vanne
- Conduite de refoulement
- Conduite primaire L= 322 m
- Conduite secondaire L= 208 m
- Tel rampe (ø50 mm)
- Lignes de gouttes et sens
- Sens d'écoulement dans les petites rampes
- Piste d'accès
- Piste périmétrale
- Drain ou Fossé
- TALUS

TABLEAU DE COORDONNEES DES SOMMETS DE LA POLYGONALE

MATRICULE	X	Y	Z
B.1	324008.5279	733881.9071	101.4303
B.1	324067.5578	734038.0699	102.2703
B.2	323981.2211	734075.6180	106.6363
B.3	323852.1441	734107.4171	104.9893
B.4	323701.5273	734147.3983	102.2542
B.6	323642.3778	733983.9797	101.9092
B.7	323692.1076	733969.1443	100.2722
B.8	323785.8776	733938.7321	101.6922